


Kit Perfis

Estruturar

FRENTE (1 : 15)

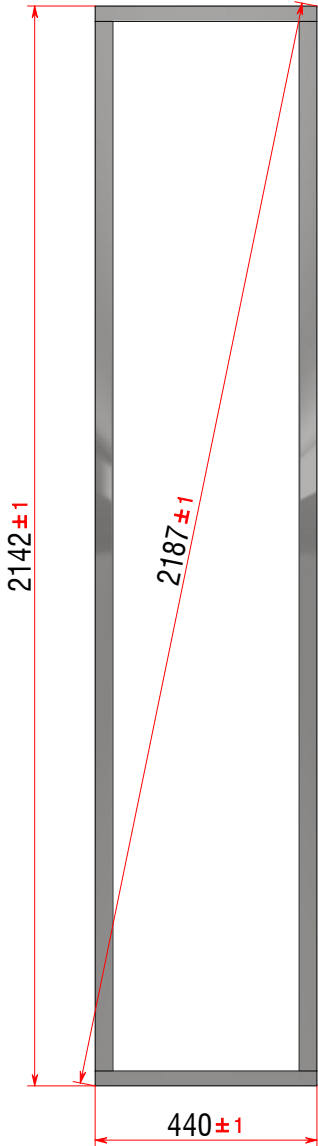


Corte de Perfis


ITEM 1 (1 : 15)



ISOMÉTRICO (1 : 15)

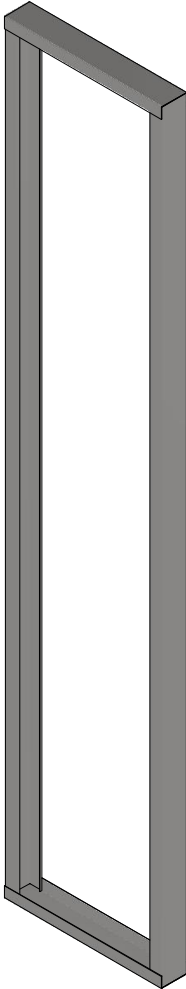

ITEM 2 (1 : 15)

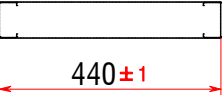


1	M70-09-2140	2	Montante - 70 x 0,90 x 2140 mm	A.1	Produção - REV 01 Escala 1:20	19/08/2025
2	R70-09-440	2	Raia - 72 x 0,90 x 440 mm	A	Protótipo - REV 01 Escala 1:20	09/07/2025
ITEM	PART NUMBER	ITEM QTY	DESCRIPTION	REV	DESCRIPTION	DATE
REVISION HISTORY						


	Project	ISCTE	Designed by	Ricardo Sá	01/07/2025
	DWG NO	ISCTE_PG01K	Drawn by	Ricardo Sá	08/09/2025
 First angle projection General Tolerances ISO 2768-cK All dimensions in mm	Description	Parede Geral 01K	Approval by	Paulo Guimarães	08/09/2025
	This drawing is property of BluFab being forbidden to its reproduction or communication third without authorization of this company.			Scale	Sheet
				1 : 15	1 of 3

Kit Placas


Corte

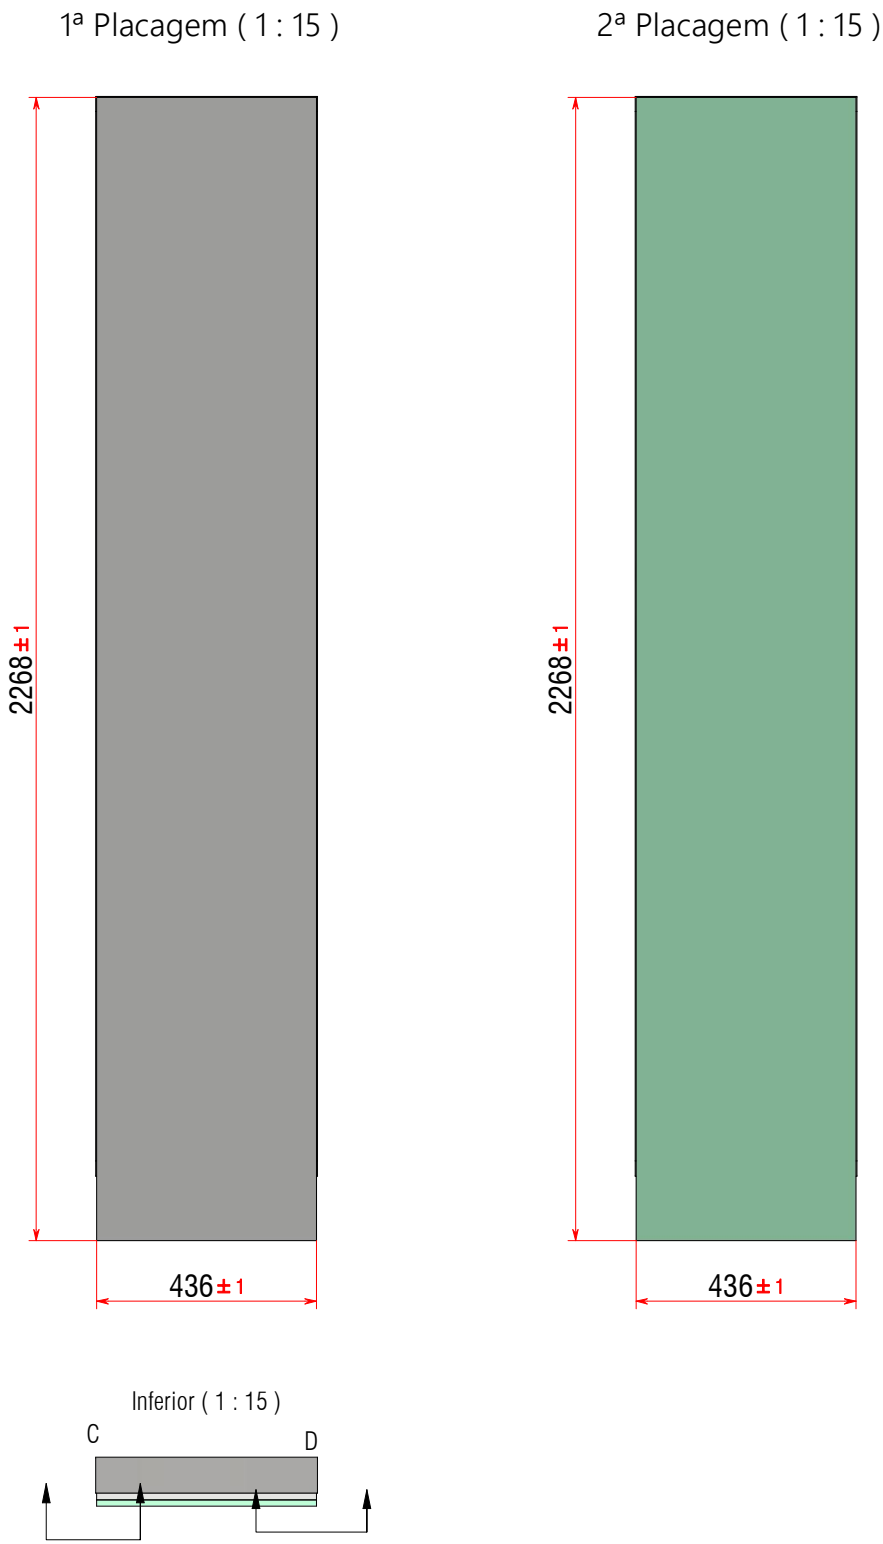

Posição

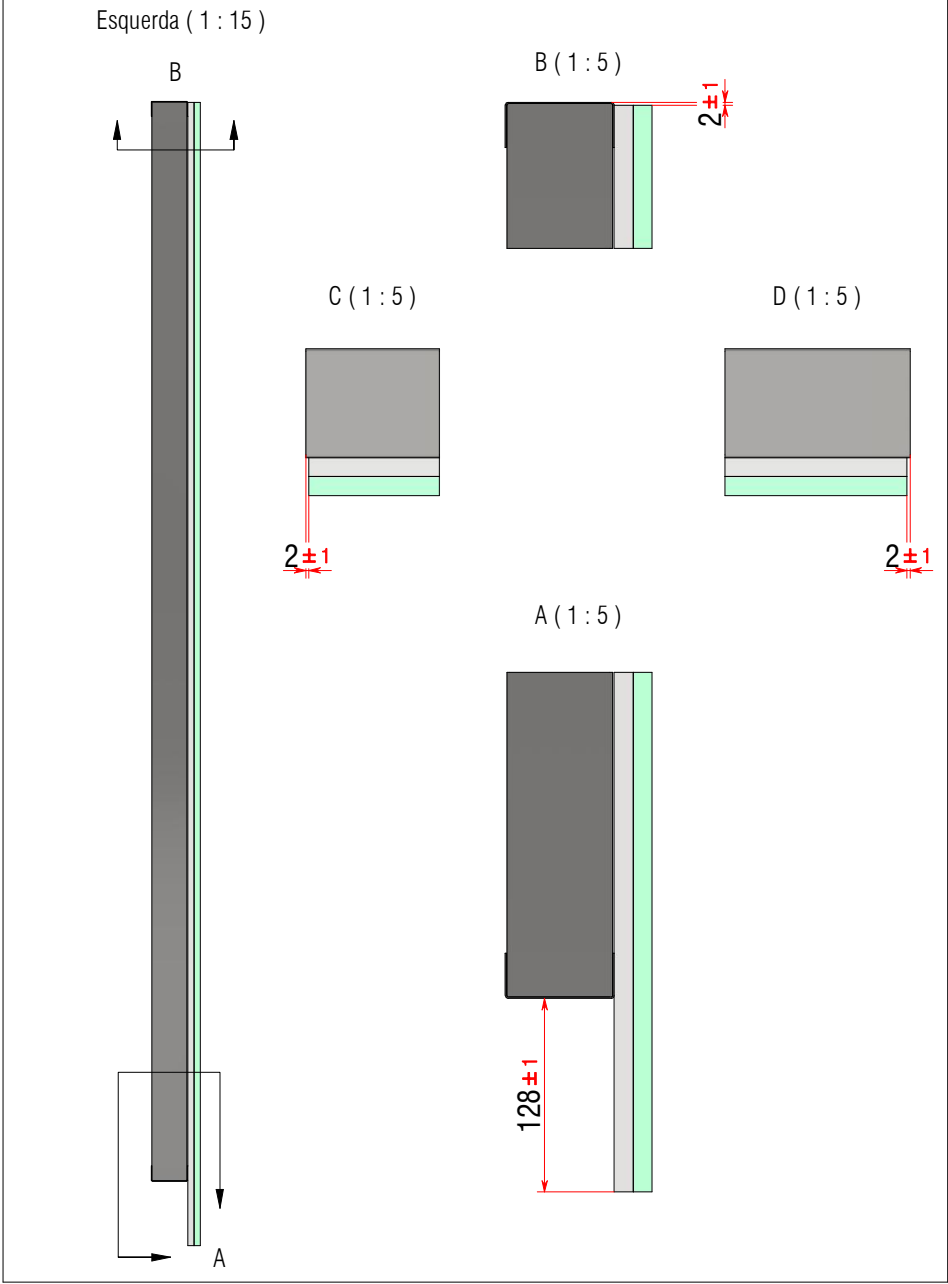

ISOMÉTRICO (1 : 15)

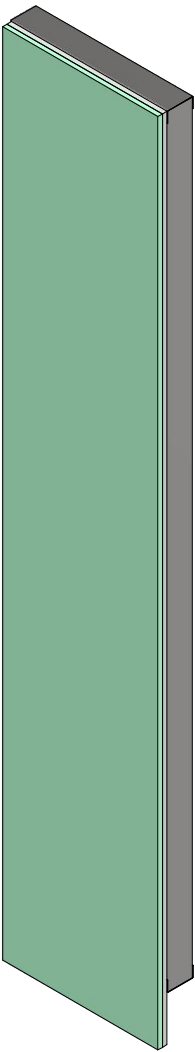

1	GGH-2268-436-12,5	1	Gyptec Gesso Standard - 2268 x 436 x 12,5 mm	A.1	Produção - REV 01 Escala 1:20	19/08/2025	BluFab First angle projection General Tolerances ISO 2768-ck All dimensions in mm Project ISCTE DWG NO ISCTE_PG01K Description Parede Geral 01K This drawing is property of BluFab being forbidden to its reproduction or communication third without authorization of this company. Designed by Ricardo Sá Drawn by Ricardo Sá Approval by Paulo Guimarães Scale 1 : 15 Sheet 2 of 3
2	GGH-2268-436-12,5	1	Gyptec Gesso Hidrofugo - 2268 x 436 x 12,5 mm	A	Protótipo - REV 01 Escala 1:20	09/07/2025	
ITEM	PART NUMBER	ITEM QTY	DESCRIPTION	REV	DESCRIPTION	DATE	
REVISION HISTORY							






D

C

D

C

B

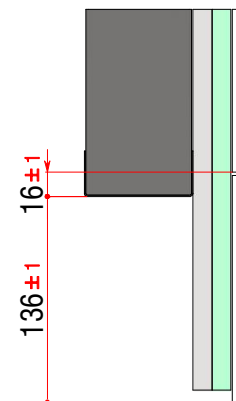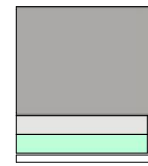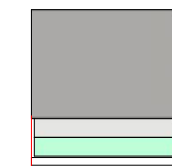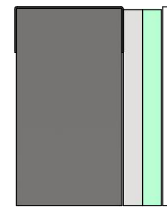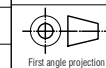A.1REVA

General Tolerances
ISO 2768-ck