


Kit Perfis


Estrutural

FRENTE (1 : 15)

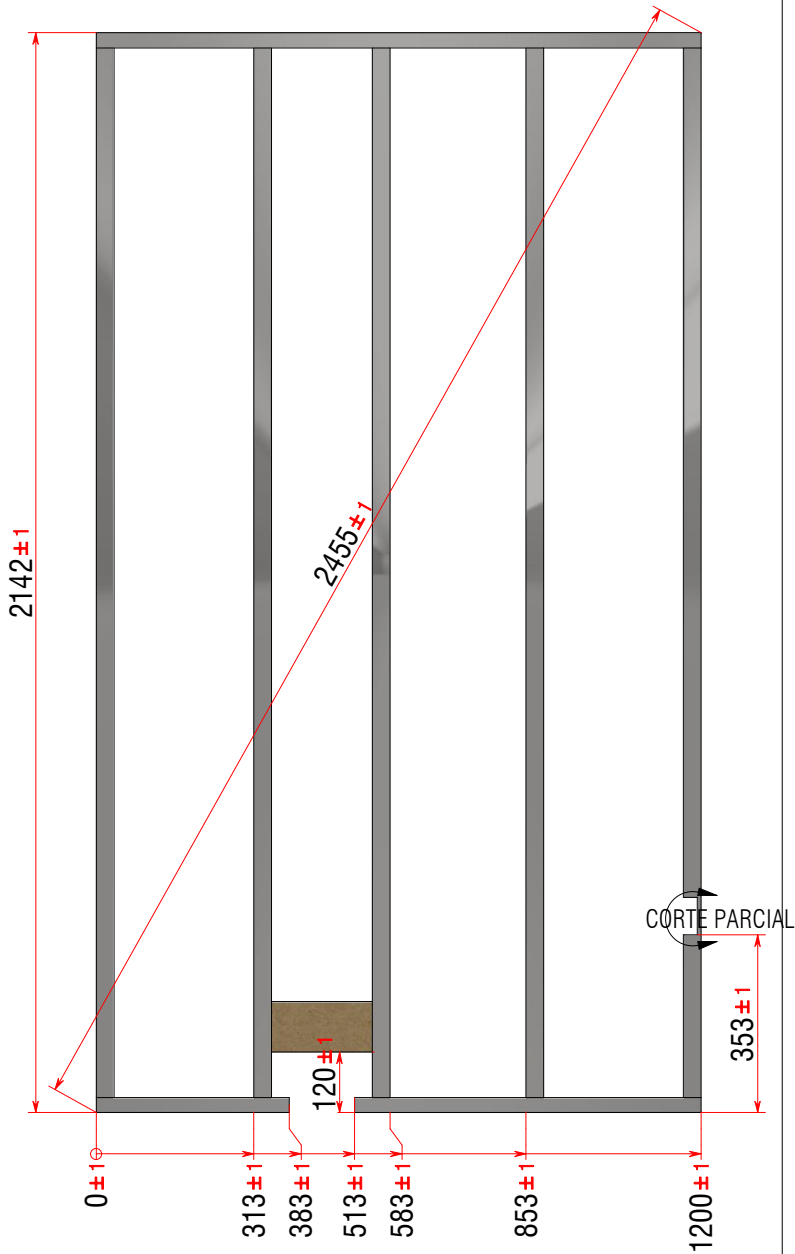


Corte de Perfis


ITEM 1 (1 : 15)

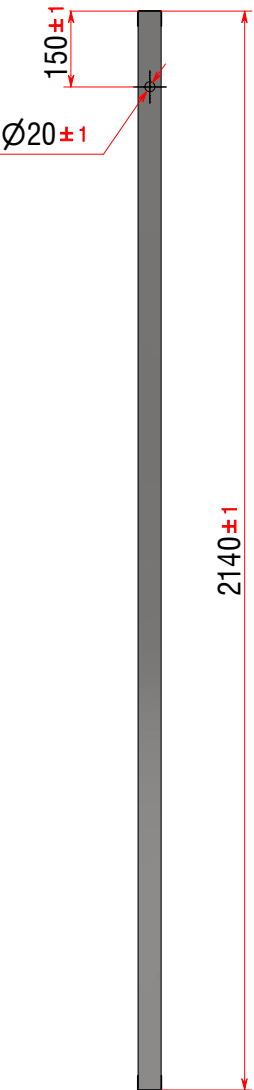


CORTE PARCIAL (1 : 2)

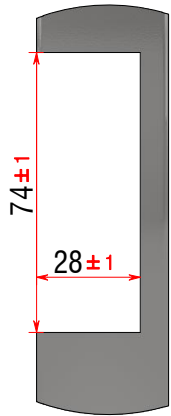


ISOMÉTRICO (1 : 15)

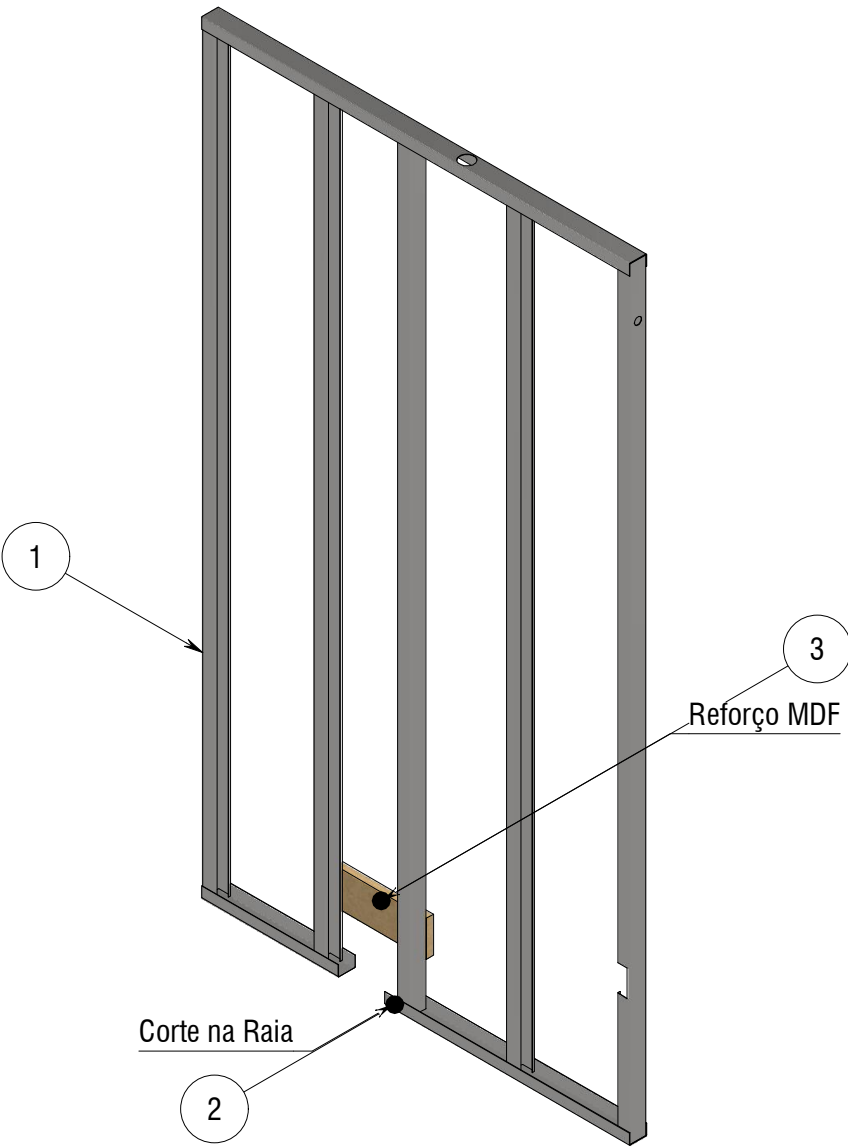

ITEM 2 (1 : 15)

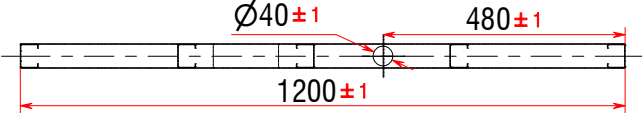

ITEM 3 (1 : 10)

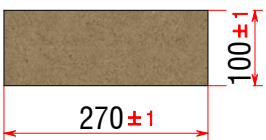

1	M48-09-2140	5	Montante - 46 x 0,90 x 2140 mm
2	R48-09-1200	2	Raia - 48 x 0,90 x 1200 mm
3	MDF-270-100-20,0	1	MDF - 270 x 100 x 20,0 mm
ITEM	PART NUMBER	ITEM QTY	DESCRIPTION

A.1	Produção - REV 01 Escala 1:20	19/08/2025
A	Protótipo - REV 01 Escala 1:20	09/07/2025
REV	DESCRIPTION	DATE
REVISION HISTORY		




	Project	ISCTE	Designed by	Ricardo Sá	03/07/2025
	DWG NO	ISCTE_PS01K	Drawn by	Ricardo Sá	29/08/2025
 First angle projection General Tolerances ISO 2768-cK All dimensions in mm	Description	Parede Sanita 01 K	Approval by	Paulo Guimarães	29/08/2025
	This drawing is property of BluFab being forbidden to its reproduction or communication third without authorization of this company.			Scale	Sheet
				1 : 15	1 of 4

Kit Placas

Corte

Posição

ISOMÉTRICO (1 : 15)

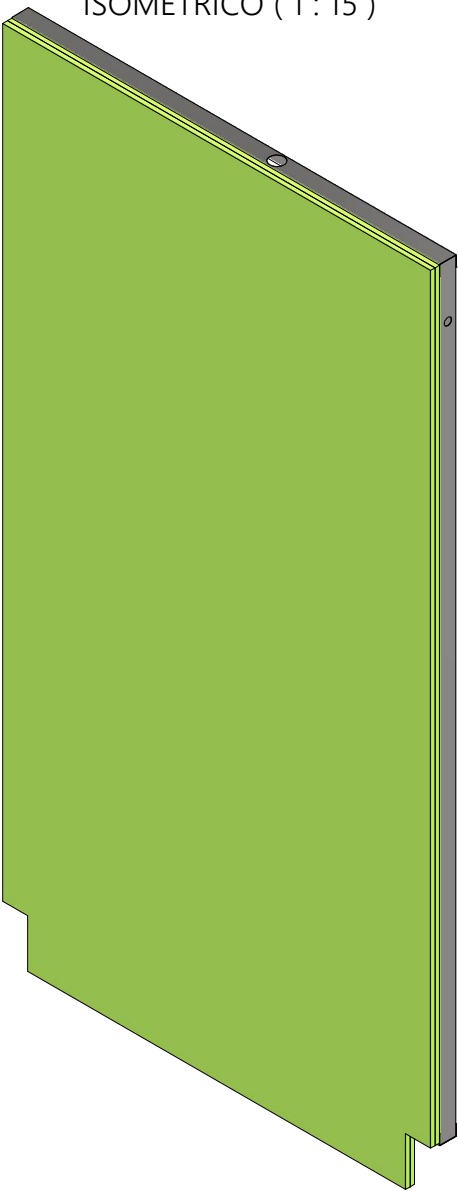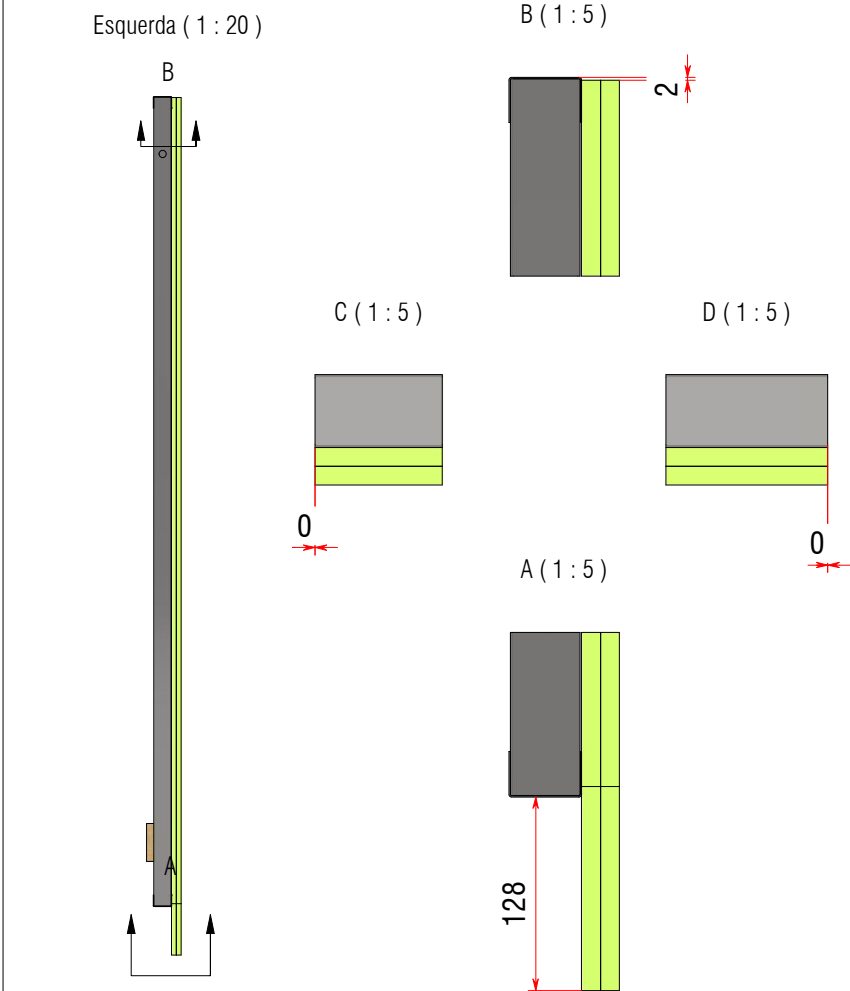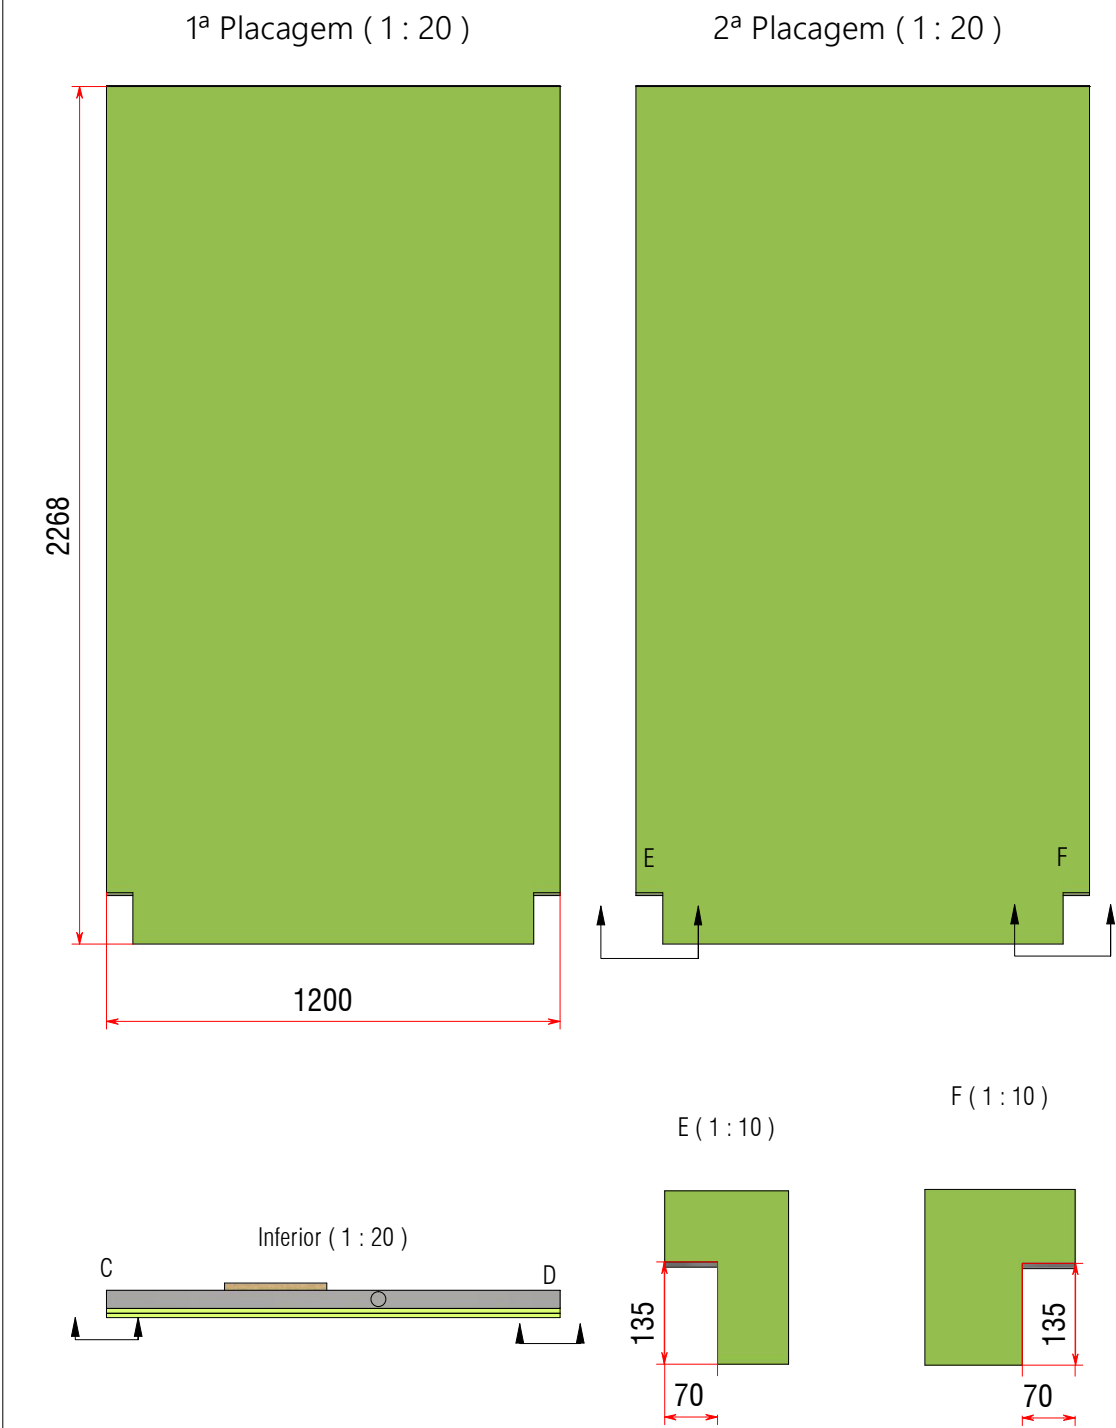

1	GGP-2268-1200-12,5	2	Gyptec Gesso Protect - 2268 x 1200 x 12,5 mm
ITEM	PART NUMBER	ITEM QTY	DESCRIPTION







A.1	Produção - REV 01 Escala 1:20	19/08/2025
A	Protótipo - REV 01 Escala 1:20	09/07/2025
REV	DESCRIPTION	DATE
REVISION HISTORY		

	Project	ISCTE	Designed by	Ricardo Sá	03/07/2025
	DWG NO	ISCTE_PS01K	Drawn by	Ricardo Sá	29/08/2025
 First angle projection General Tolerances ISO 2768-ck All dimensions in mm	Description	Parede Sanita 01 K	Approval by	Paulo Guimarães	29/08/2025
	This drawing is property of BluFab being forbidden to its reproduction or communication third without authorization of this company.				Scale 1 : 20




D

C

B

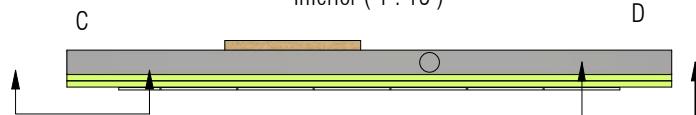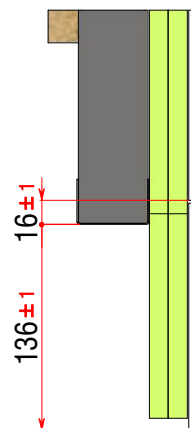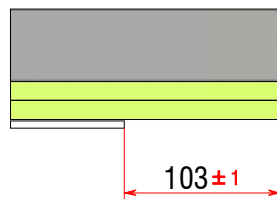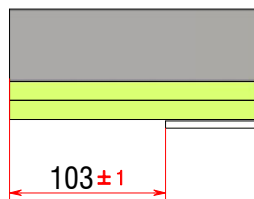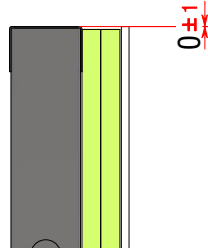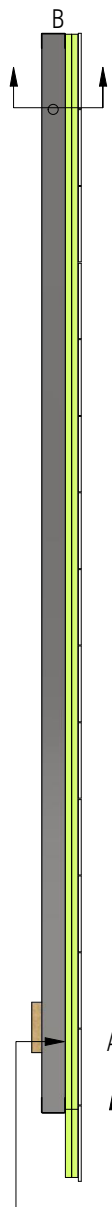


D

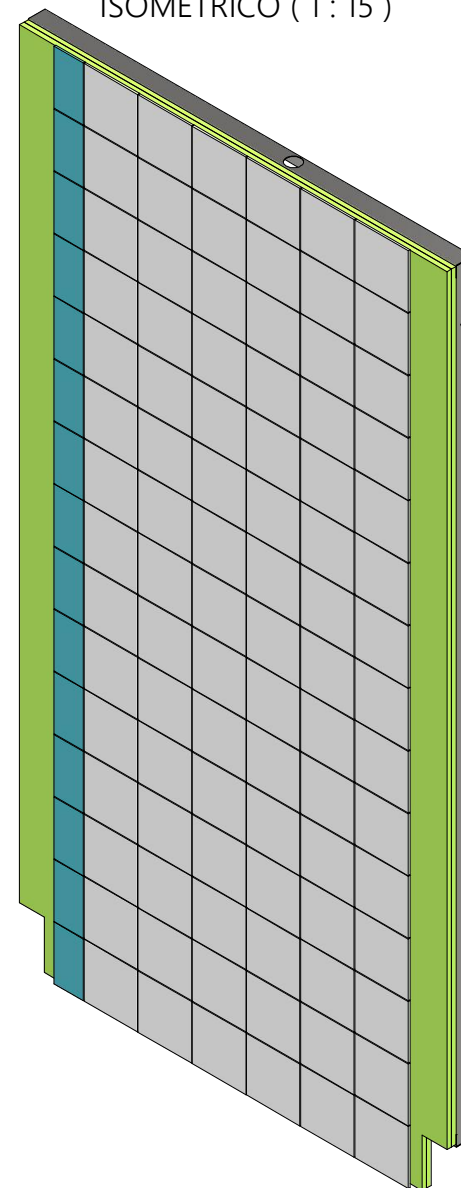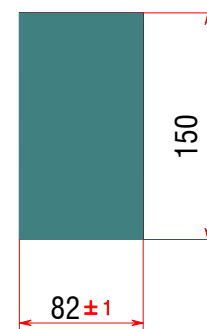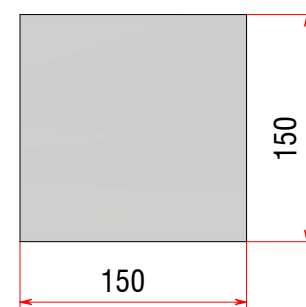A


Kit Furação

Frente (1 : 15)

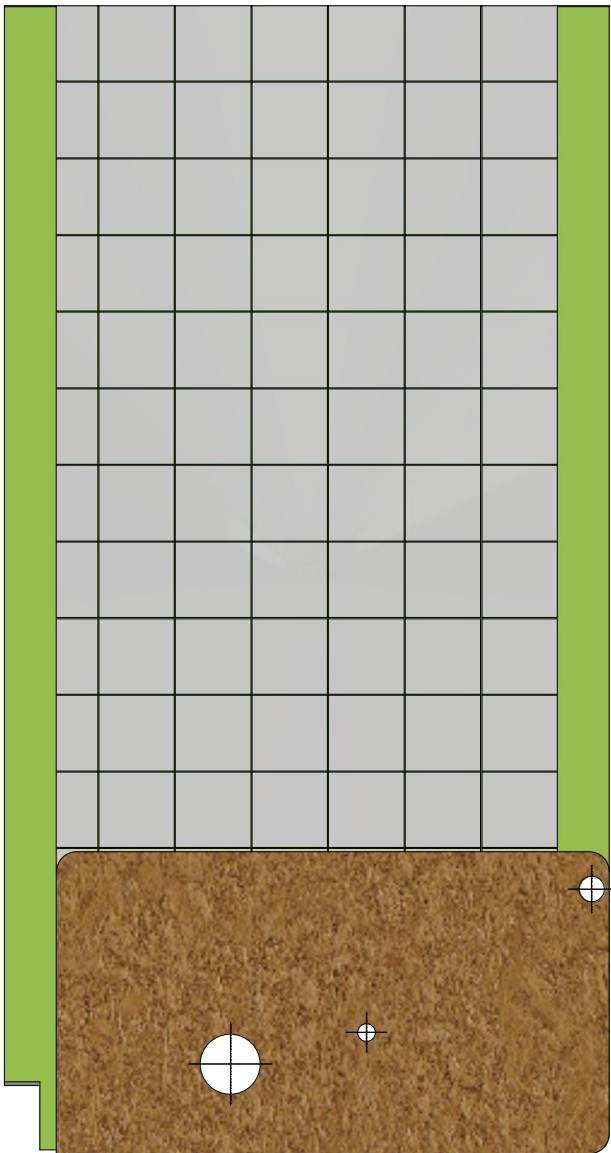

Ponto 0 Gab 03

ISOMÉTRICO (1 : 15)

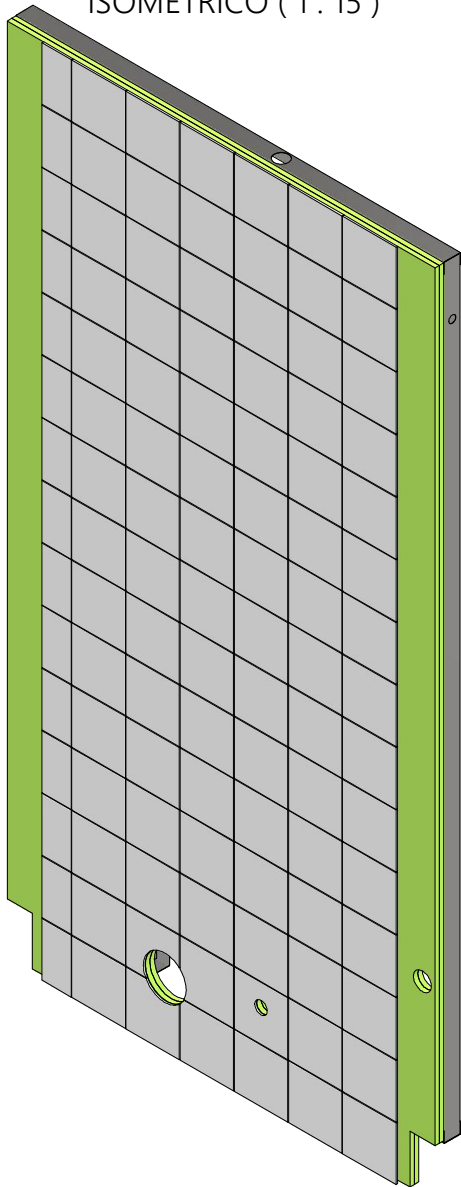

ITEM	PART NUMBER	ITEM QTY	DESCRIPTION
------	-------------	----------	-------------

A.1	Produção - REV 01 Escala 1:20	19/08/2025
A	Protótipo - REV 01 Escala 1:20	09/07/2025
REV	DESCRIPTION	DATE
REVISION HISTORY		

	Project	ISCTE	Designed by	Ricardo Sá	03/07/2025
	DWG NO	ISCTE_PS01K	Drawn by	Ricardo Sá	29/08/2025
	Description	Parede Sanita 01 K	Approval by	Paulo Guimarães	29/08/2025
	This drawing is property of BluFab being forbidden to its reproduction or communication third without authorization of this company.			Scale	Sheet
First angle projection				1 : 15	4 of 4
General Tolerances ISO 2768-ck					
All dimensions in mm					