



Kit Perfis

Estruturar


FRENTE (1 : 15)

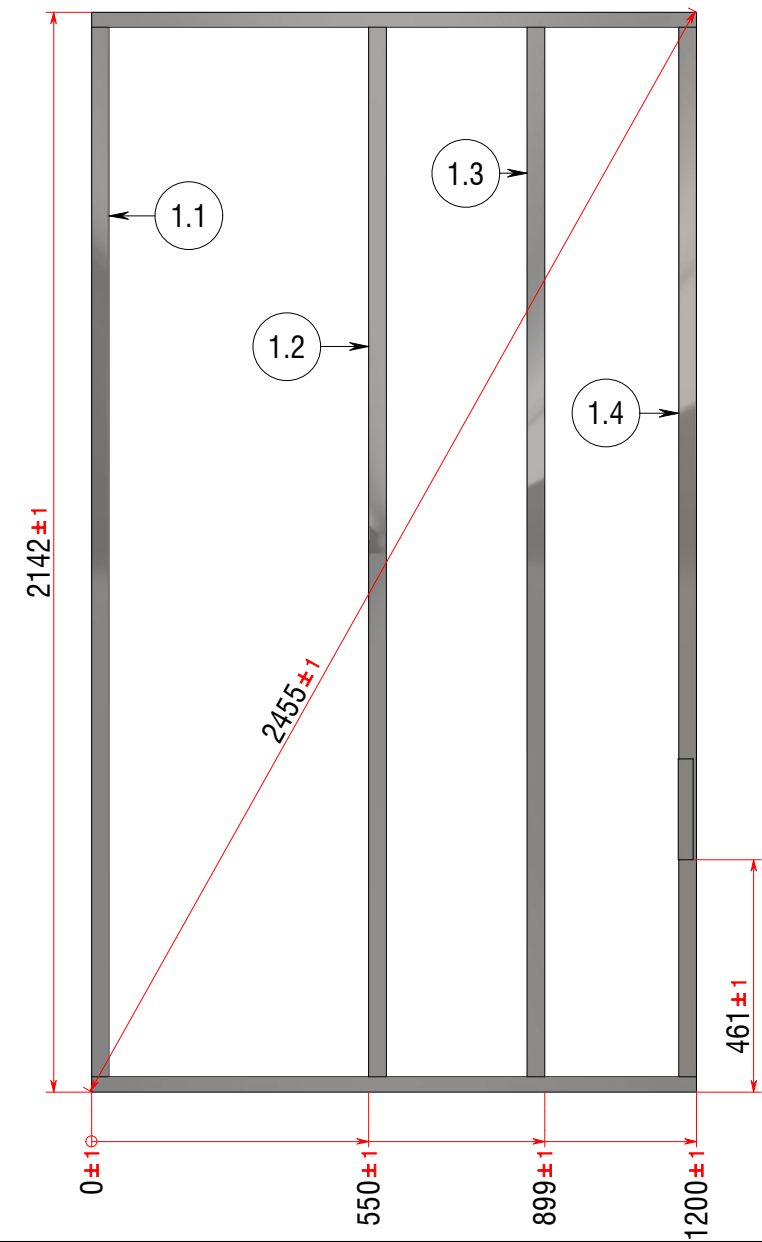


ITEM 2 (1 : 15)

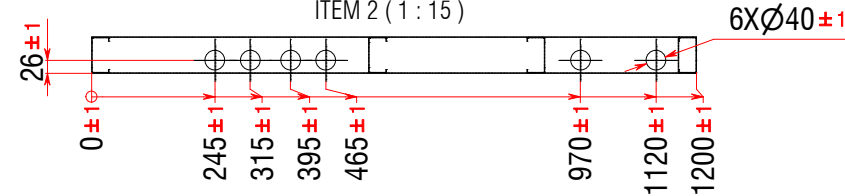


Corte
de
Perfis

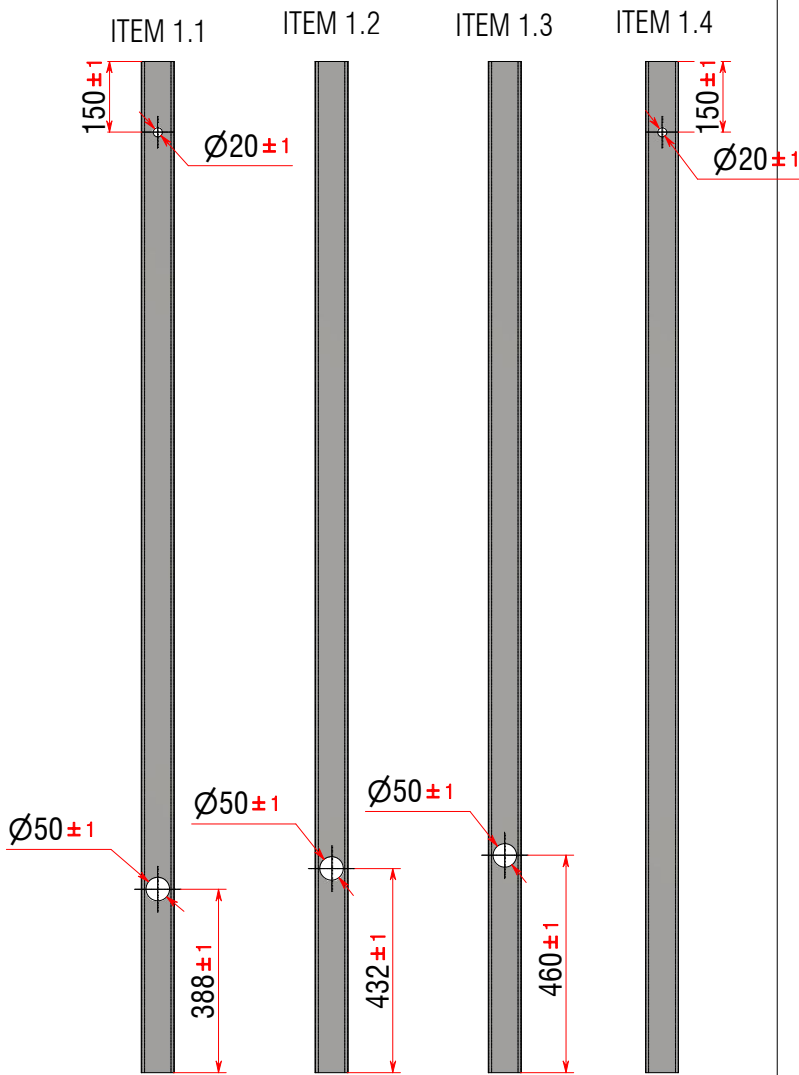

ITEM 3 (1 : 15)

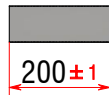

ISOMÉTRICO (1 : 15)

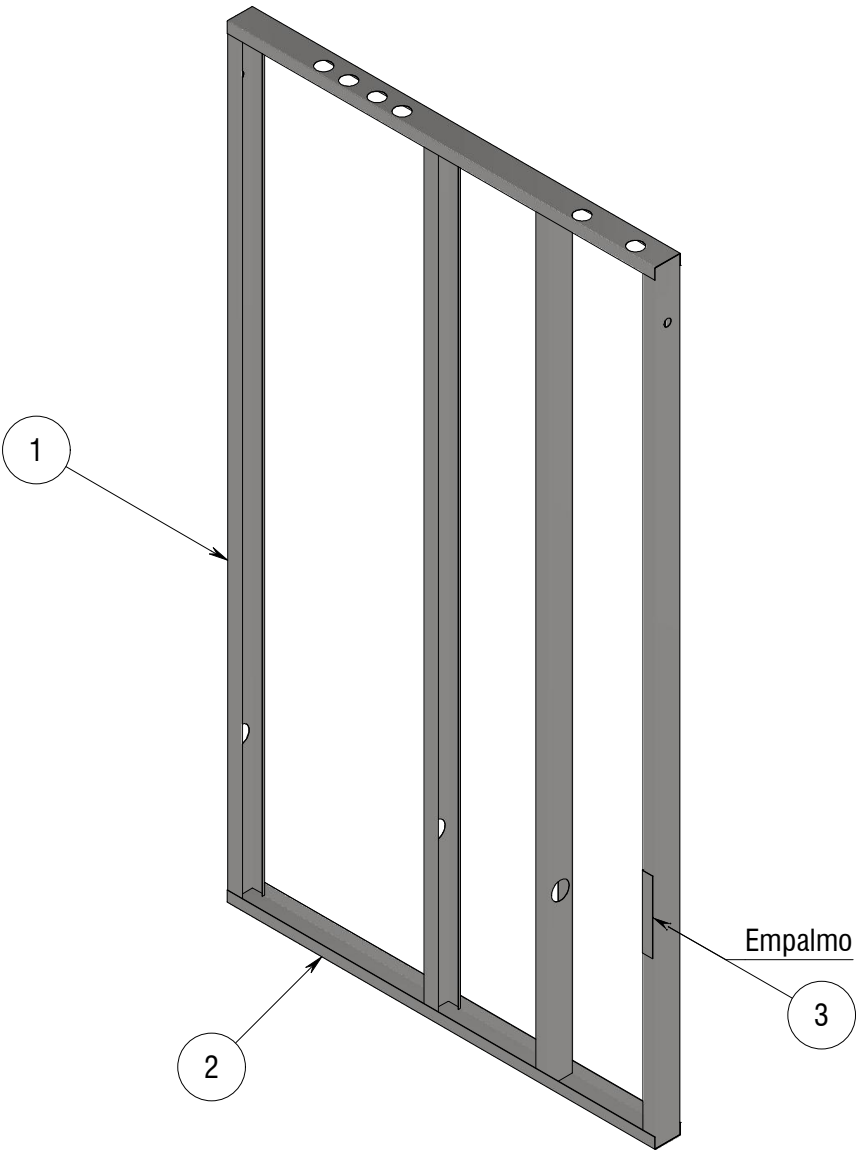

1	M70-09-2140	4	Montante - 70 x 0,90 x 2140 mm
2	R70-09-1200	2	Raia - 72 x 0,90 x 1200 mm
3	R70-09-200	1	Raia - 72 x 0,90 x 200 mm
ITEM	PART NUMBER	ITEM QTY	DESCRIPTION

A.1	Produção - REV 01 Escala 1:20	19/08/2025
A	Protótipo - REV 01 Escala 1:20	09/07/2025
REV	DESCRIPTION	DATE
REVISION HISTORY		




	Project	ISCTE	Designed by	Ricardo Sá	03/07/2025
	DWG NO	ISCTE_PL01K	Drawn by	Ricardo Sá	29/08/2025
 First angle projection General Tolerances ISO 2768-ck All dimensions in mm	Description	Painel de Lavatório 01K	Approval by	Paulo Guimarães	29/08/2025
	This drawing is property of BluFab being forbidden to its reproduction or communication third without authorization of this company.				Scale 1 : 15

Kit Placas

Corte

Posição

ISOMÉTRICO (1 : 15)

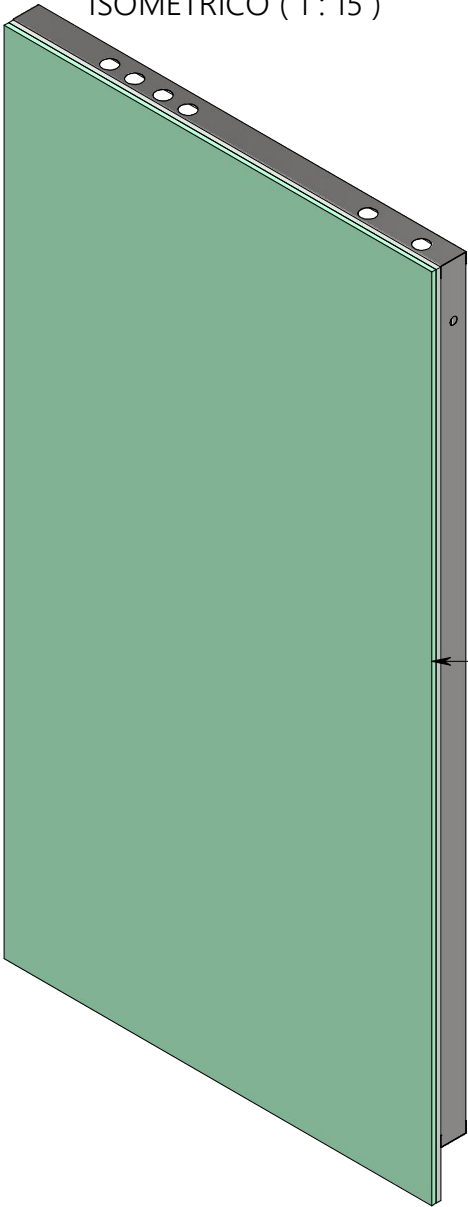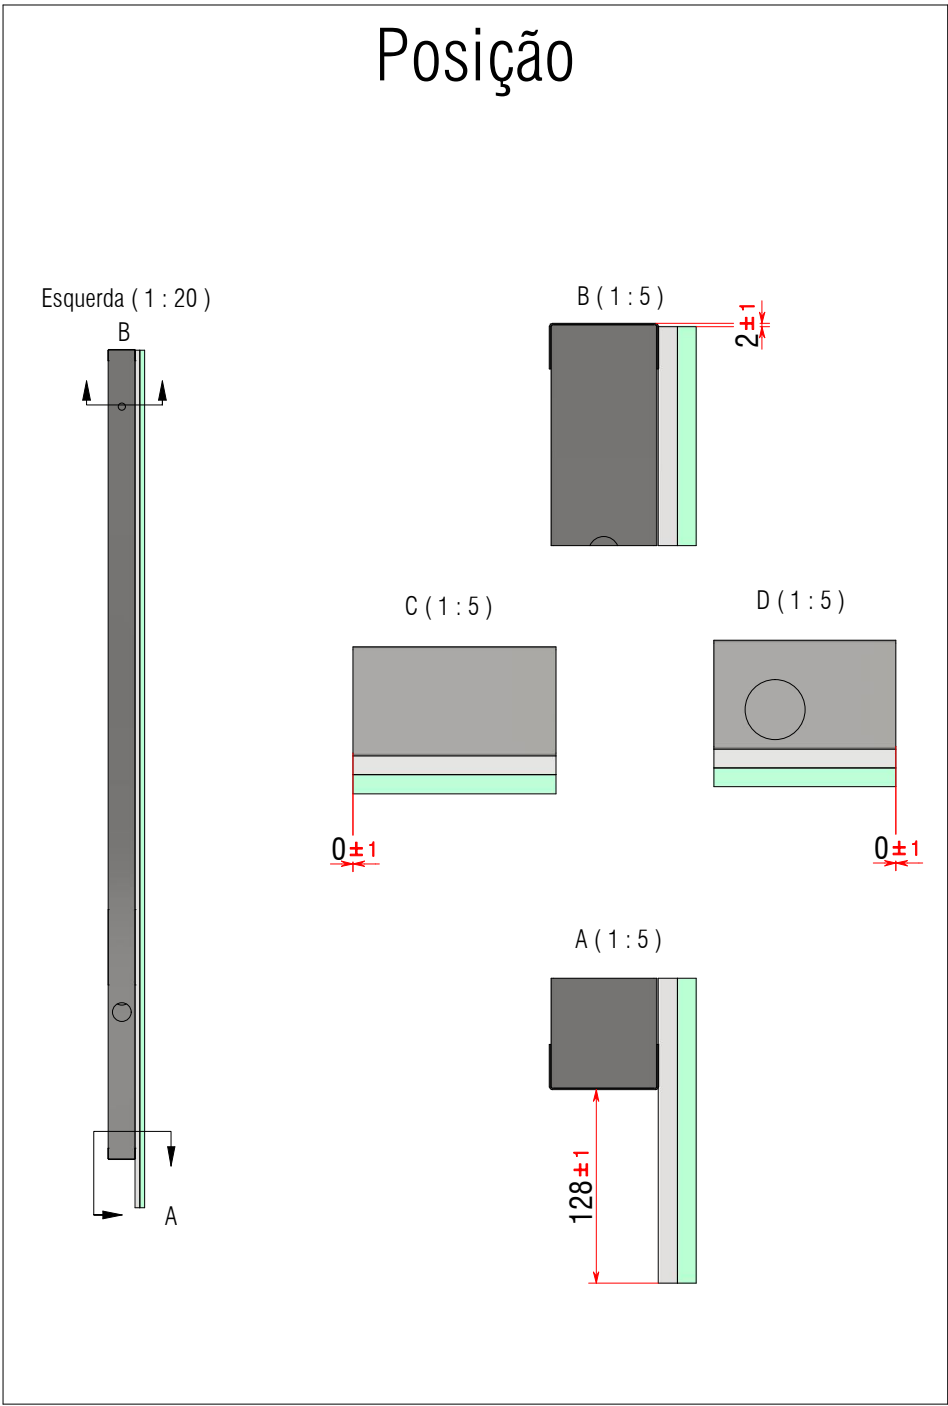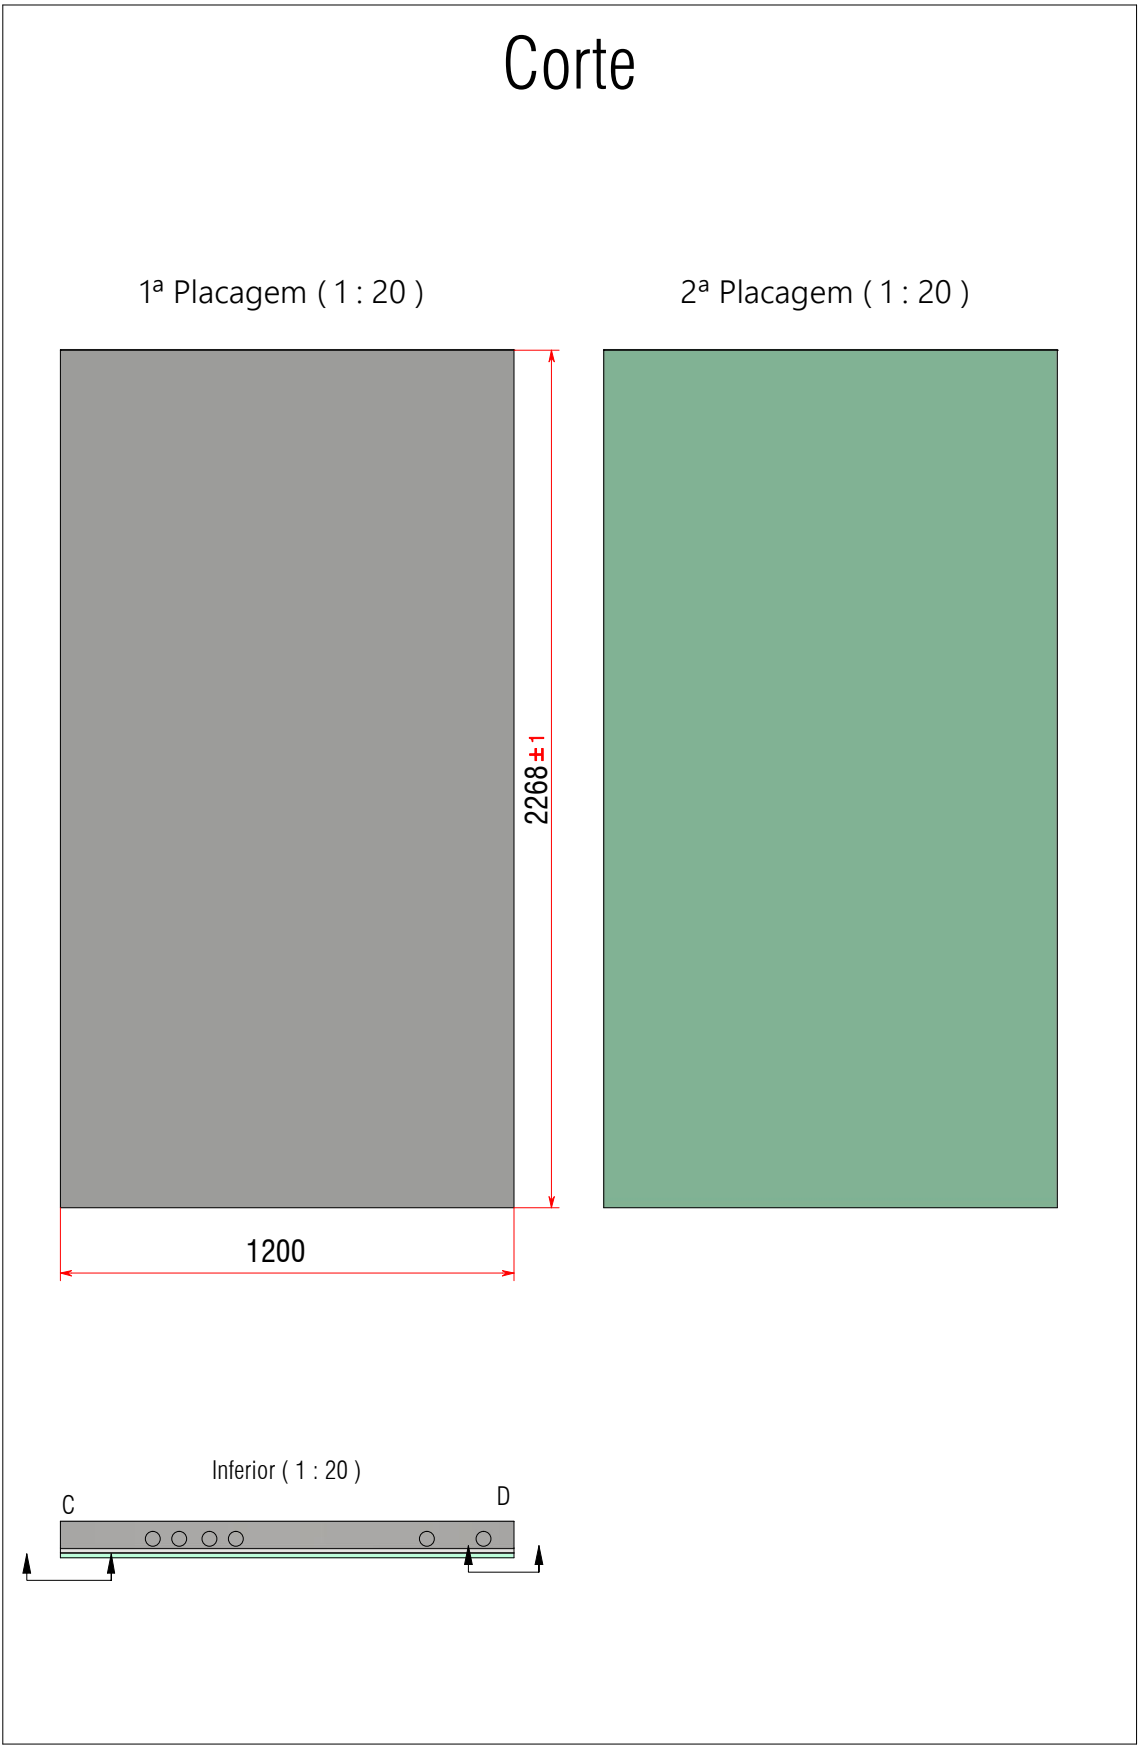


Usar Gabari de corte para H's


							BluFab First angle projection General Tolerances ISO 2768-ck All dimensions in mm	Project	ISCTE	Designed by	Ricardo Sá	03/07/2025
1	GGS-2268-1200-12,5	1	Gyptec Gesso Standard - 2268 x 1200 x 12,5 mm	A.1	Produção - REV 01 Escala 1:20	19/08/2025		DWG NO	ISCTE_PL01K	Drawn by	Ricardo Sá	29/08/2025
2	GGH-2268-1200-12,5	1	Gyptec Gesso Hidrofugo - 2268 x 1200 x 12,5 mm	A	Protótipo - REV 01 Escala 1:20	09/07/2025		Description	Painel de Lavatório 01K	Approval by	Paulo Guimarães	29/08/2025
ITEM	PART NUMBER	ITEM QTY	DESCRIPTION	REV	DESCRIPTION	DATE		This drawing is property of BluFab being forbidden to its reproduction or communication third without authorization of this company.			Scale	Sheet
						REVISION HISTORY			1 : 20		2 of 4	

Kit Cerâmicos


Posição

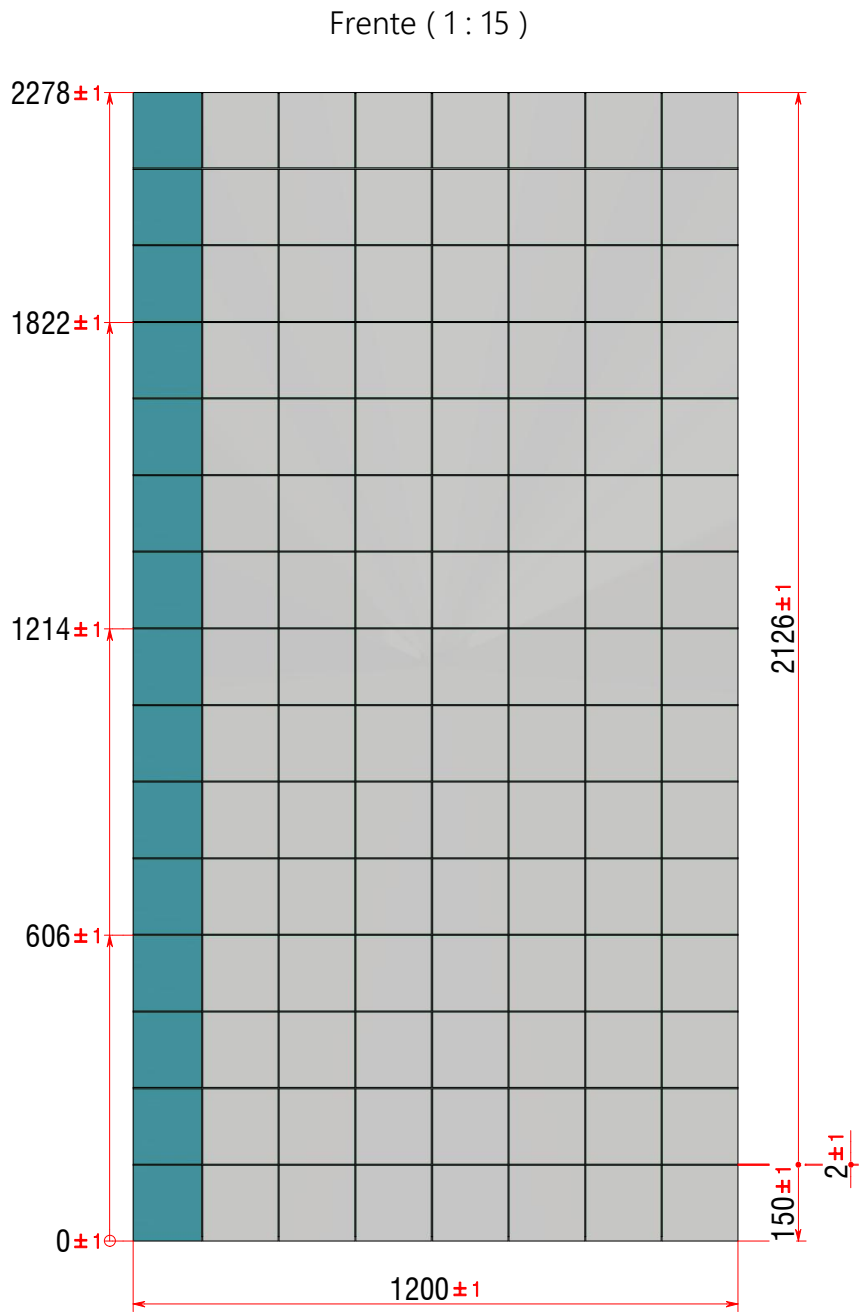


Esquerda (1 : 15)

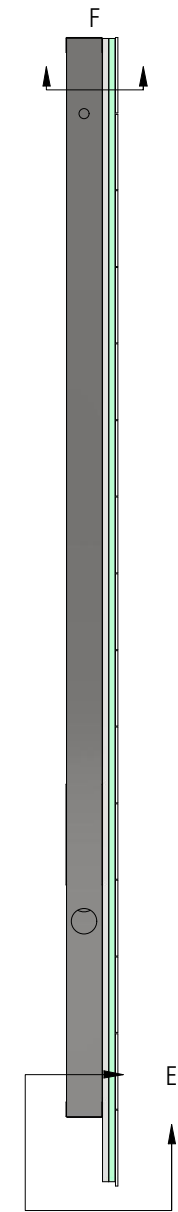


F (1 : 5)

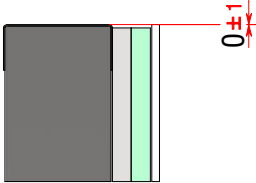


G (1 : 5)

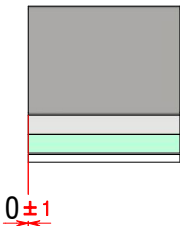


H (1 : 5)

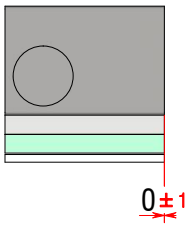

E (1 : 5)

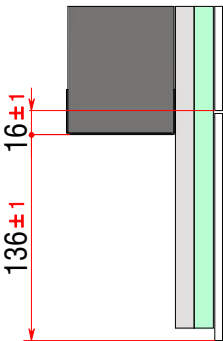


Inferior (1 : 15)

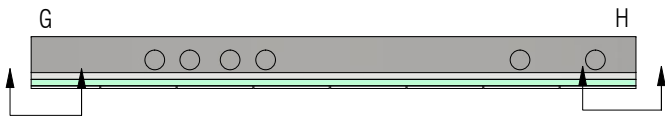


Corte


ITEM 4 (1 : 5)

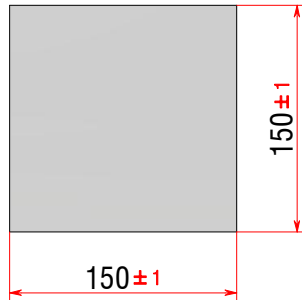

ITEM 5 (1 : 5)

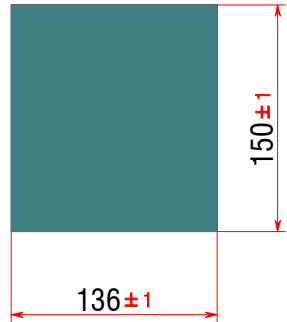

ISOMÉTRICO (1 : 15)

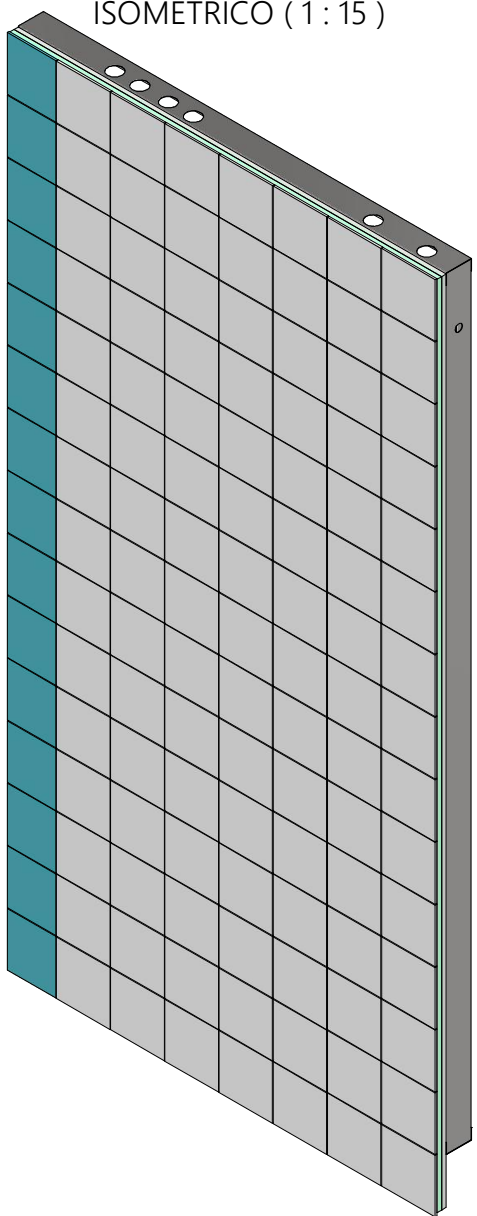


1	PVB-A-150-150-5,0	105	Primus Victoria Branco - A - 150 x 150 x 5,0 mm
2	PVB-A-136-150-5,0	15	Primus Victoria Branco - A - 136 x 150 x 5,0 mm
ITEM	PART NUMBER	ITEM QTY	DESCRIPTION

A.1	Produção - REV 01 Escala 1:20	19/08/2025
A	Protótipo - REV 01 Escala 1:20	09/07/2025
REV	DESCRIPTION	DATE
REVISION HISTORY		

	Project	ISCTE	Designed by	Ricardo Sá	03/07/2025
	DWG NO	ISCTE_PL01K	Drawn by	Ricardo Sá	29/08/2025
 First angle projection General Tolerances ISO 2768-ck All dimensions in mm	Description	Painel de Lavatório 01K	Approval by	Paulo Guimarães	29/08/2025
	This drawing is property of BluFab being forbidden to its reproduction or communication third without authorization of this company.				Scale 1 : 15

Kit Furação


Frente (1 : 15)

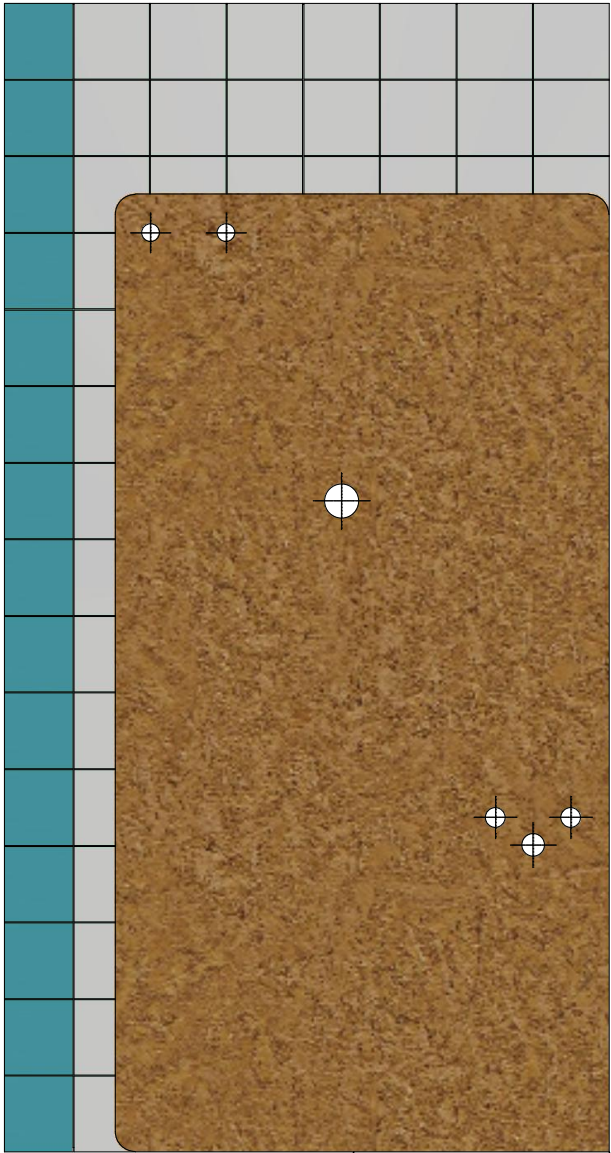

Gab 04

Ponto 0

ISOMÉTRICO (1 : 15)

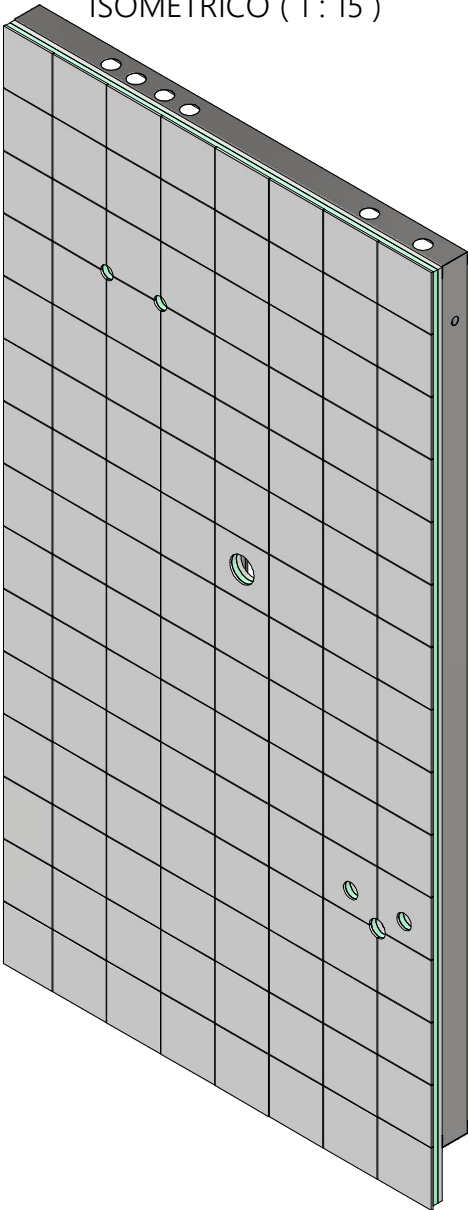

ITEM	PART NUMBER	ITEM QTY	DESCRIPTION
------	-------------	----------	-------------

A.1	Produção - REV 01 Escala 1:20	19/08/2025
A	Protótipo - REV 01 Escala 1:20	09/07/2025
REV	DESCRIPTION	DATE
REVISION HISTORY		

	Project	ISCTE	Designed by	Ricardo Sá	03/07/2025
	DWG NO	ISCTE_PL01K	Drawn by	Ricardo Sá	29/08/2025
 First angle projection General Tolerances ISO 2768-ck All dimensions in mm	Description	Painel de Lavatório 01K	Approval by	Paulo Guimarães	29/08/2025
	This drawing is property of BluFab being forbidden to its reproduction or communication third without authorization of this company.				Scale 1 : 15